Zyra kadastrale komunale / Opštinska katastarska kancelarija: Ferizaj

Zona kadastrale / Katastarska zona: Babush I Serbëve

Lloji i njësisë kadastrale / Vrsta katastarske jedinice : Parcel

Nr. i njësisë kadastrale / Br. katastarske jedinice : 00629-1

Numri i lëndës / Broj predmeta:

Shkalla e zvoglimit / Razmera plana : 1:2000


Republika e Kosovës

Republika Kosova-Republic of Kosova

Qeveria -Vlada-Government

Ministria e Mjedisit dhe Planifikimit Hapësinor /Ministarstvo Sredine i Prostornog Planiranja/Ministry of Environment and Spatial Planning

AGJENCIA KADASTRALE E KOSOVËS/ KATASTARSKA AGECIJA KOSOVA/ KOSOVA CADASTRAL AGENCY

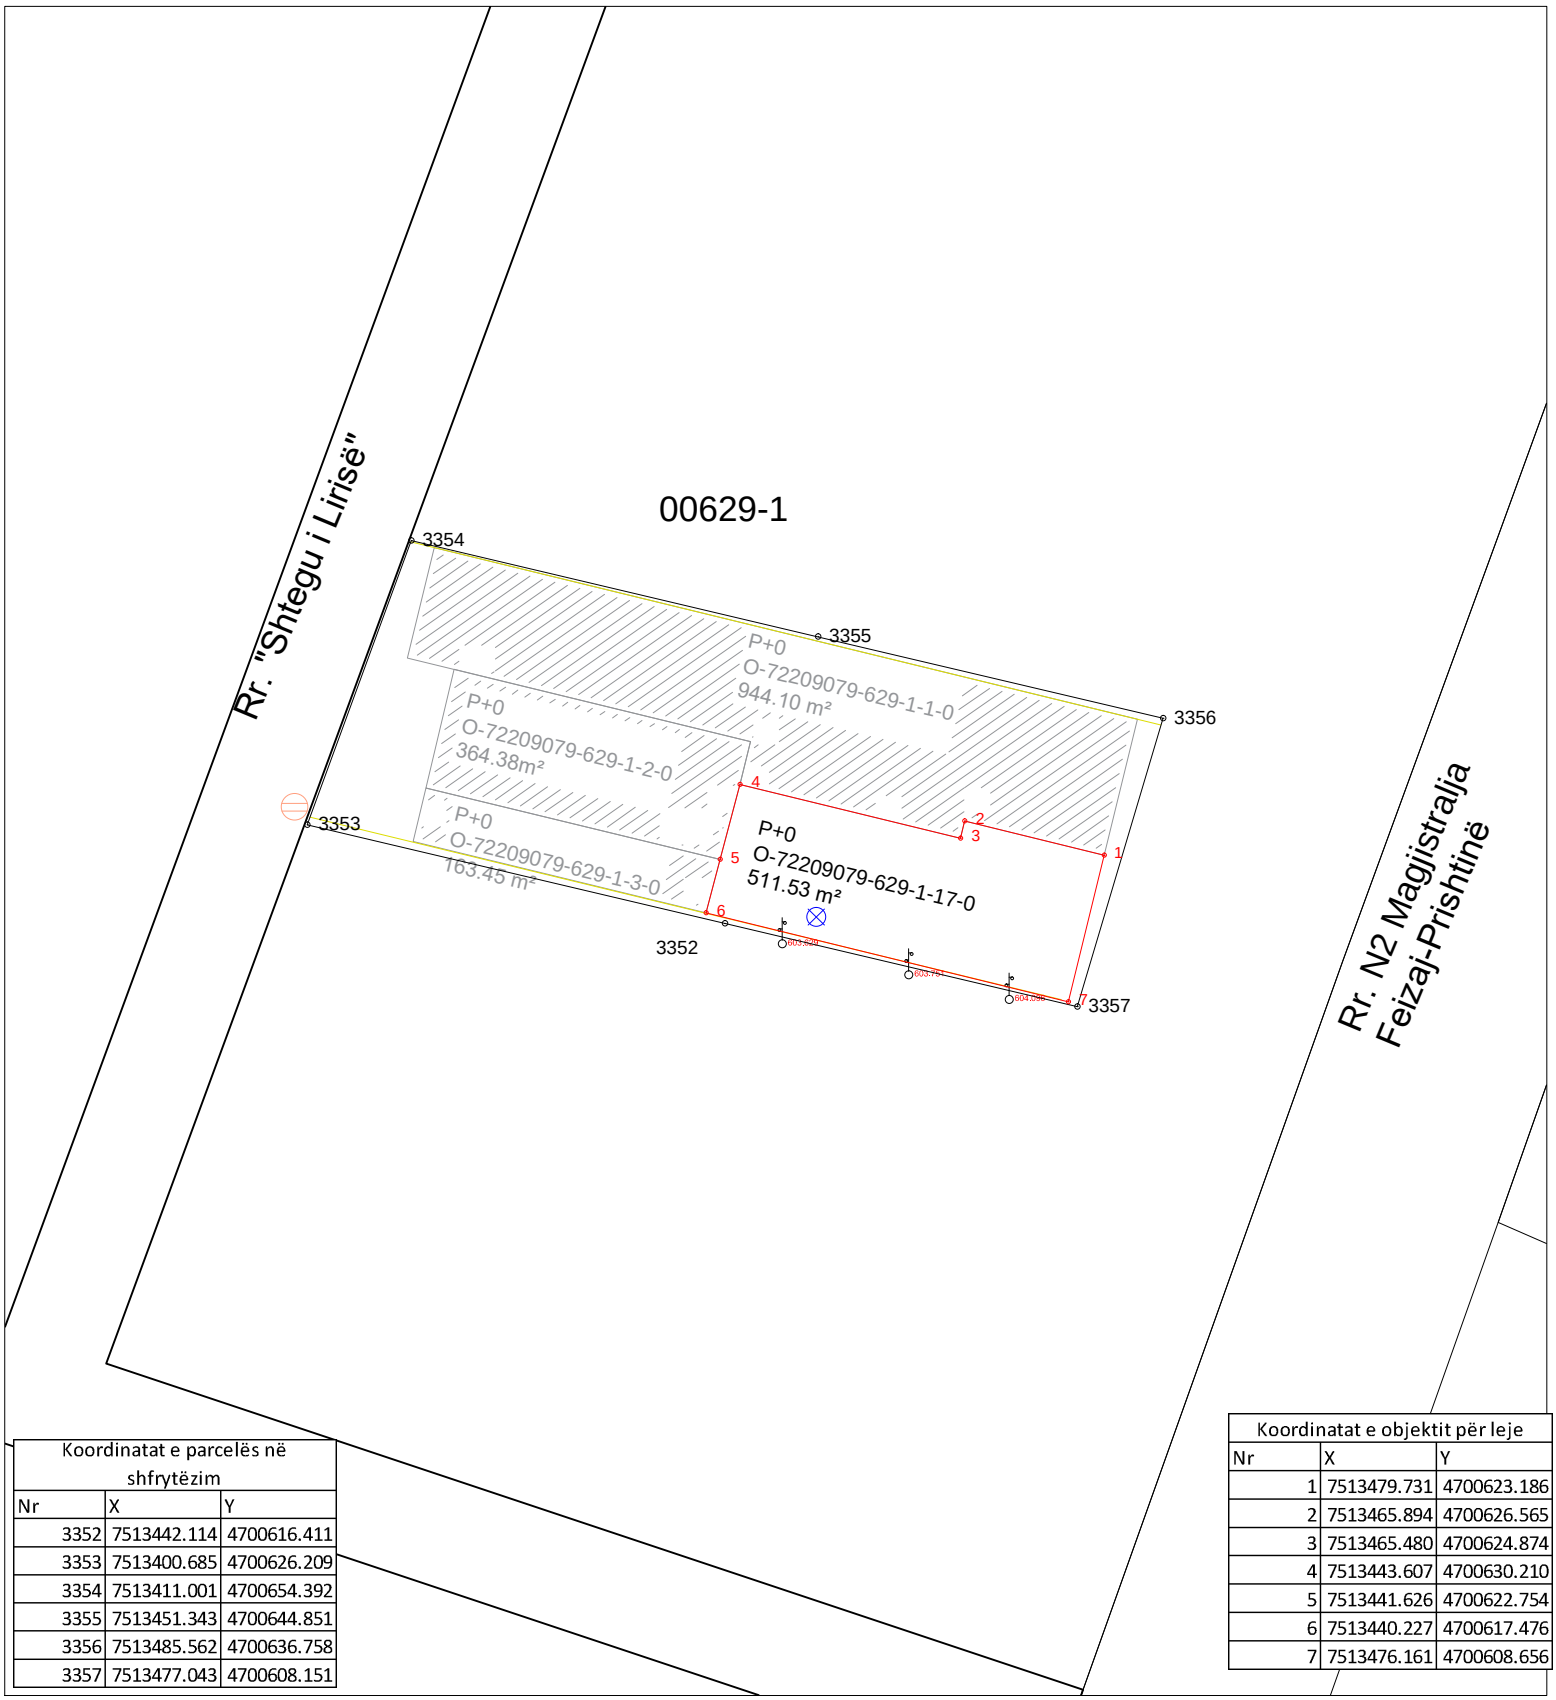

Koordinatat e parcelës në shfrytëzim		
Nr	X	Y
3352	7513442.114	4700616.411
3353	7513400.685	4700626.209
3354	7513411.001	4700654.392
3355	7513451.343	4700644.851
3356	7513485.562	4700636.758
3357	7513477.043	4700608.151

Koordinatat e objektit për leje		
Nr	X	Y
1	7513479.731	4700623.186
2	7513465.894	4700626.565
3	7513465.480	4700624.874
4	7513443.607	4700630.210
5	7513441.626	4700622.754
6	7513440.227	4700617.476
7	7513476.161	4700608.656

Rilevoi / Snimio: LIRIDON SEJDIU

(emri dhe mbiemri i gjeodetit/kompanisë/ ime i prezime geodeta/ kompanije)

Nr. i licencës / Br. licence: 140

Nënshkrimi / Potpis:

Data e rilevimit / Datum snimanja: 18.06.2024

V.V.

Aprovoi / Usvojio:

(emri dhe mbiemri i përsonit zyrtar/ ime i prezime sluzbenog lica)

Nënshkrimi / Potpis:

Data e aprovimit / Datum usvajanja: