Zyra kadastrale komunale / Opštinska katastarska kancelarija: Ferizaj

Zona kadastrale / Katastarska zona: Babush I Serbëve

Lloji i njësisë kadastrale / Vrsta katastarske jedinice : Ndërtesë

Nr. i njësisë kadastrale / Br. katastarske jedinice : 00629-1

228/2026

Numri i lëndës / Broj predmeta: 260/1172-140/26

Shkalla e zvoglimit / Razmera plana : 1:2000


Republika e Kosovës

Republika Kosova-Republic of Kosova

Qeveria -Vlada-Government

Ministria e Mjedisit dhe Planifikimit Hapësinor /Ministarstvo Sredine i Prostornog Planiranja/Ministry of Environment and Spatial Planning

AGJENCIA KADASTRALE E KOSOVËS/ KATASTARSKA AGECIJA KOSOVA/ KOSOVA CADASTRAL AGENCY

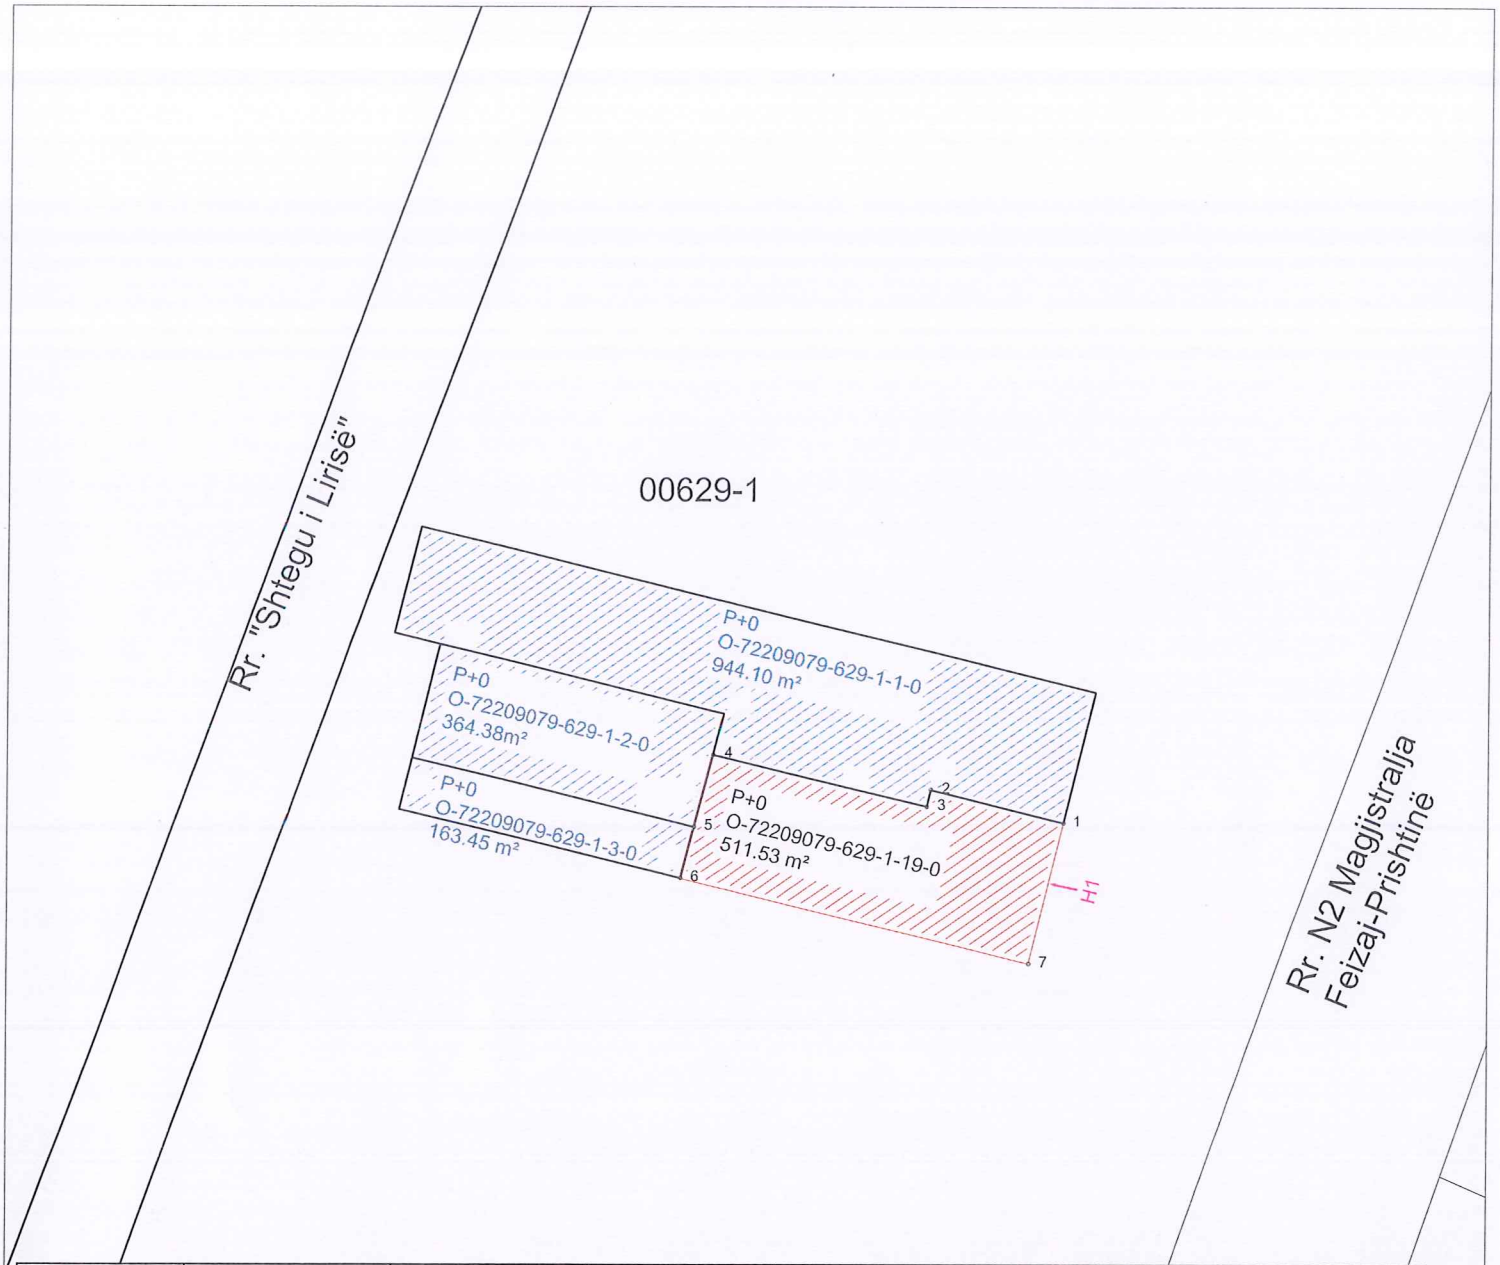

Nr	Y	X	H	Kodi	Përshkrimi	Burimi
1	7513479.731	4700623.186	603.452	20	Pikë e ndërtesës	PM
2	7513465.890	4700626.570	603.452	20	Pikë e ndërtesës	PM
3	7513465.480	4700624.870	603.452	20	Pikë e ndërtesës	PM
4	7513443.610	4700630.210	603.452	20	Pikë e ndërtesës	PM
5	7513441.630	4700622.750	603.452	20	Pikë e ndërtesës	PM
6	7513440.230	4700617.480	603.452	20	Pikë e ndërtesës	PM
7	7513476.159	4700608.649	603.452	20	Pikë e ndërtesës	PM

Rilevoi / Snimio: LIRIDON SEJDIU

(emri dhe mbiemri i gjeodetit/kompanisë/ ime i prezime geodeta/ kompanije)

Nr. i licencës / Br. licence: 140

Nënshkrimi / Potpis: _____

Data e rilevimit / Datum snimanja: 22.07.2025

LIRIDON A. SEJDIU - LICENCIRANI GEODETA - FERIZAJ-UROŠEVAC

V.V.

Aprovoi / Usvojio: _____

(emri dhe mbiemri i përsonit zyrtar/ ime i prezime sluzbenog lica)

Nënshkrimi / Potpis: _____

Data e aprovimit / Datum usvajanja: _____